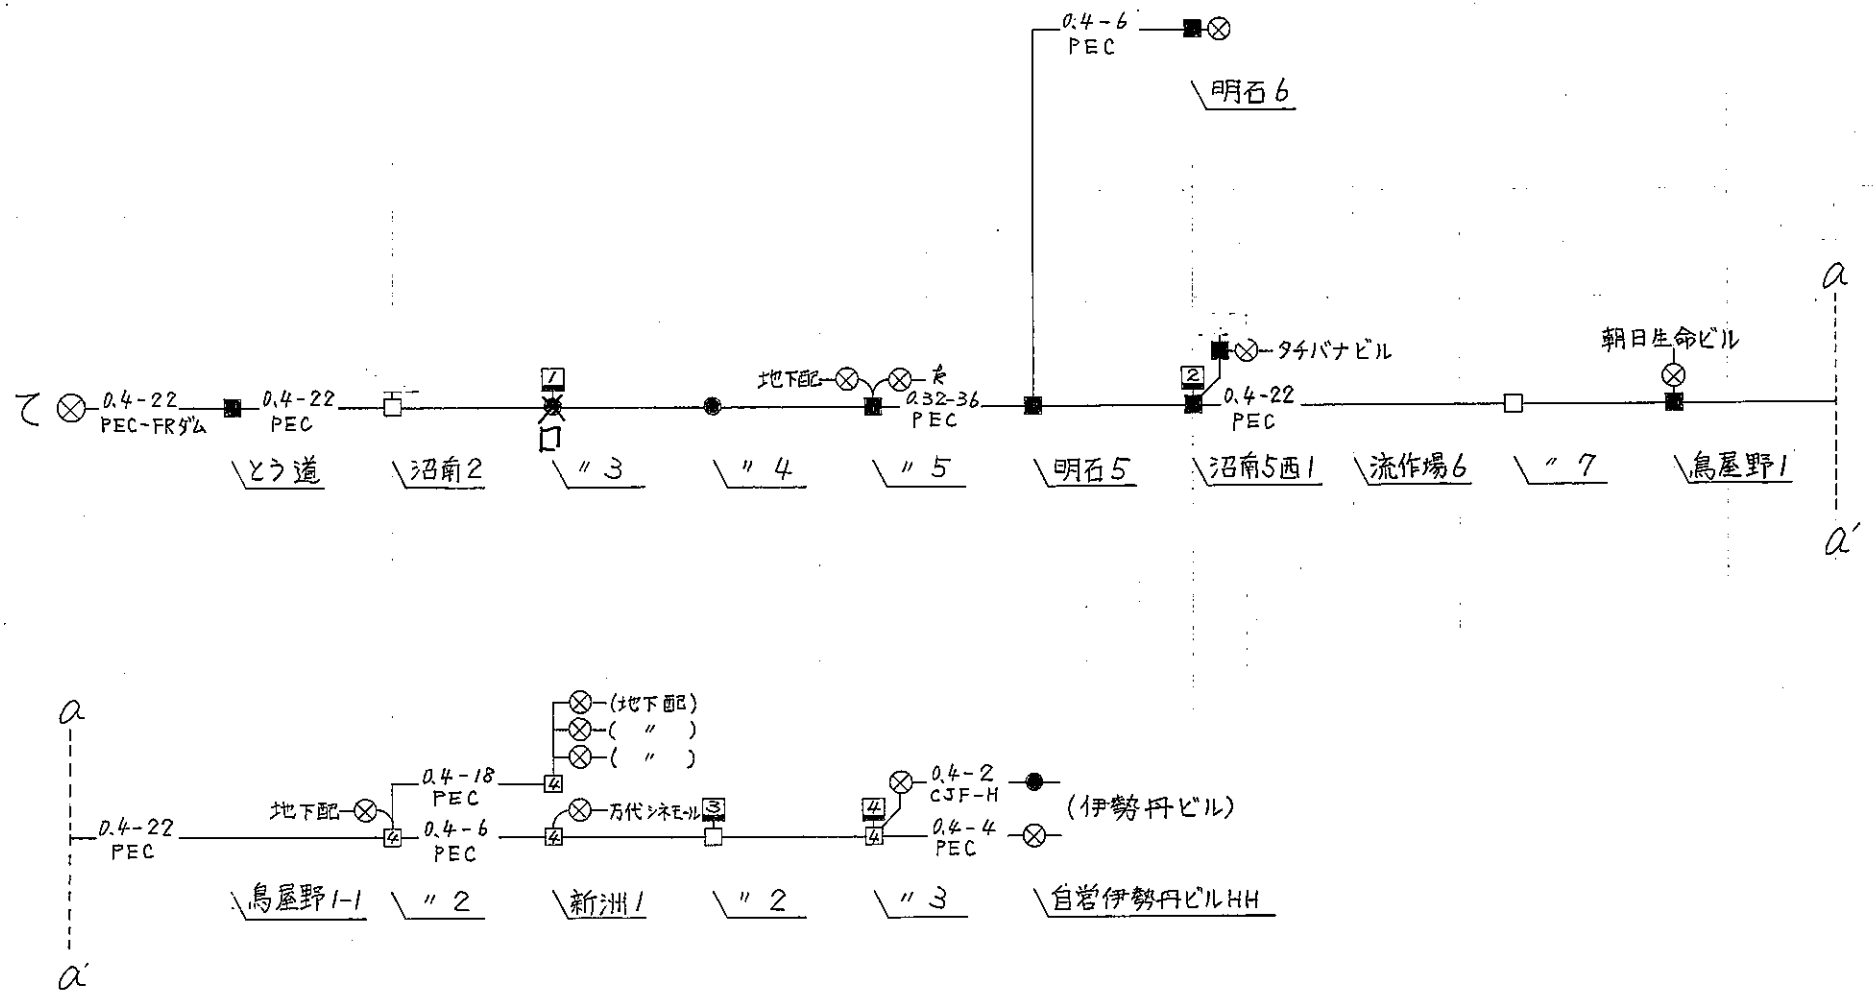
て
0.4-22
PEC-FRダム
0.4-22
PEC
とう道
沼南2
〃 3
〃 4
地下配
0.32-36
PEC
〃 5
0.4-6
PEC
明石6
明石5
タチバナビル
0.4-22
PEC
沼南5西1
流作場6
〃 7
朝日生命ビル
鳥屋野1
a
a'
a
a'
0.4-22
PEC
地下配
鳥屋野1-1
0.4-18
PEC
0.4-6
PEC
〃 2
(地下配)
(〃)
(〃)
万代シネモール
新洲1
〃 2
0.4-2
CJF-H
0.4-4
PEC
〃 3
(伊勢丹ビル)
自岩伊勢丹ビルHH

新潟東 て ケーブル