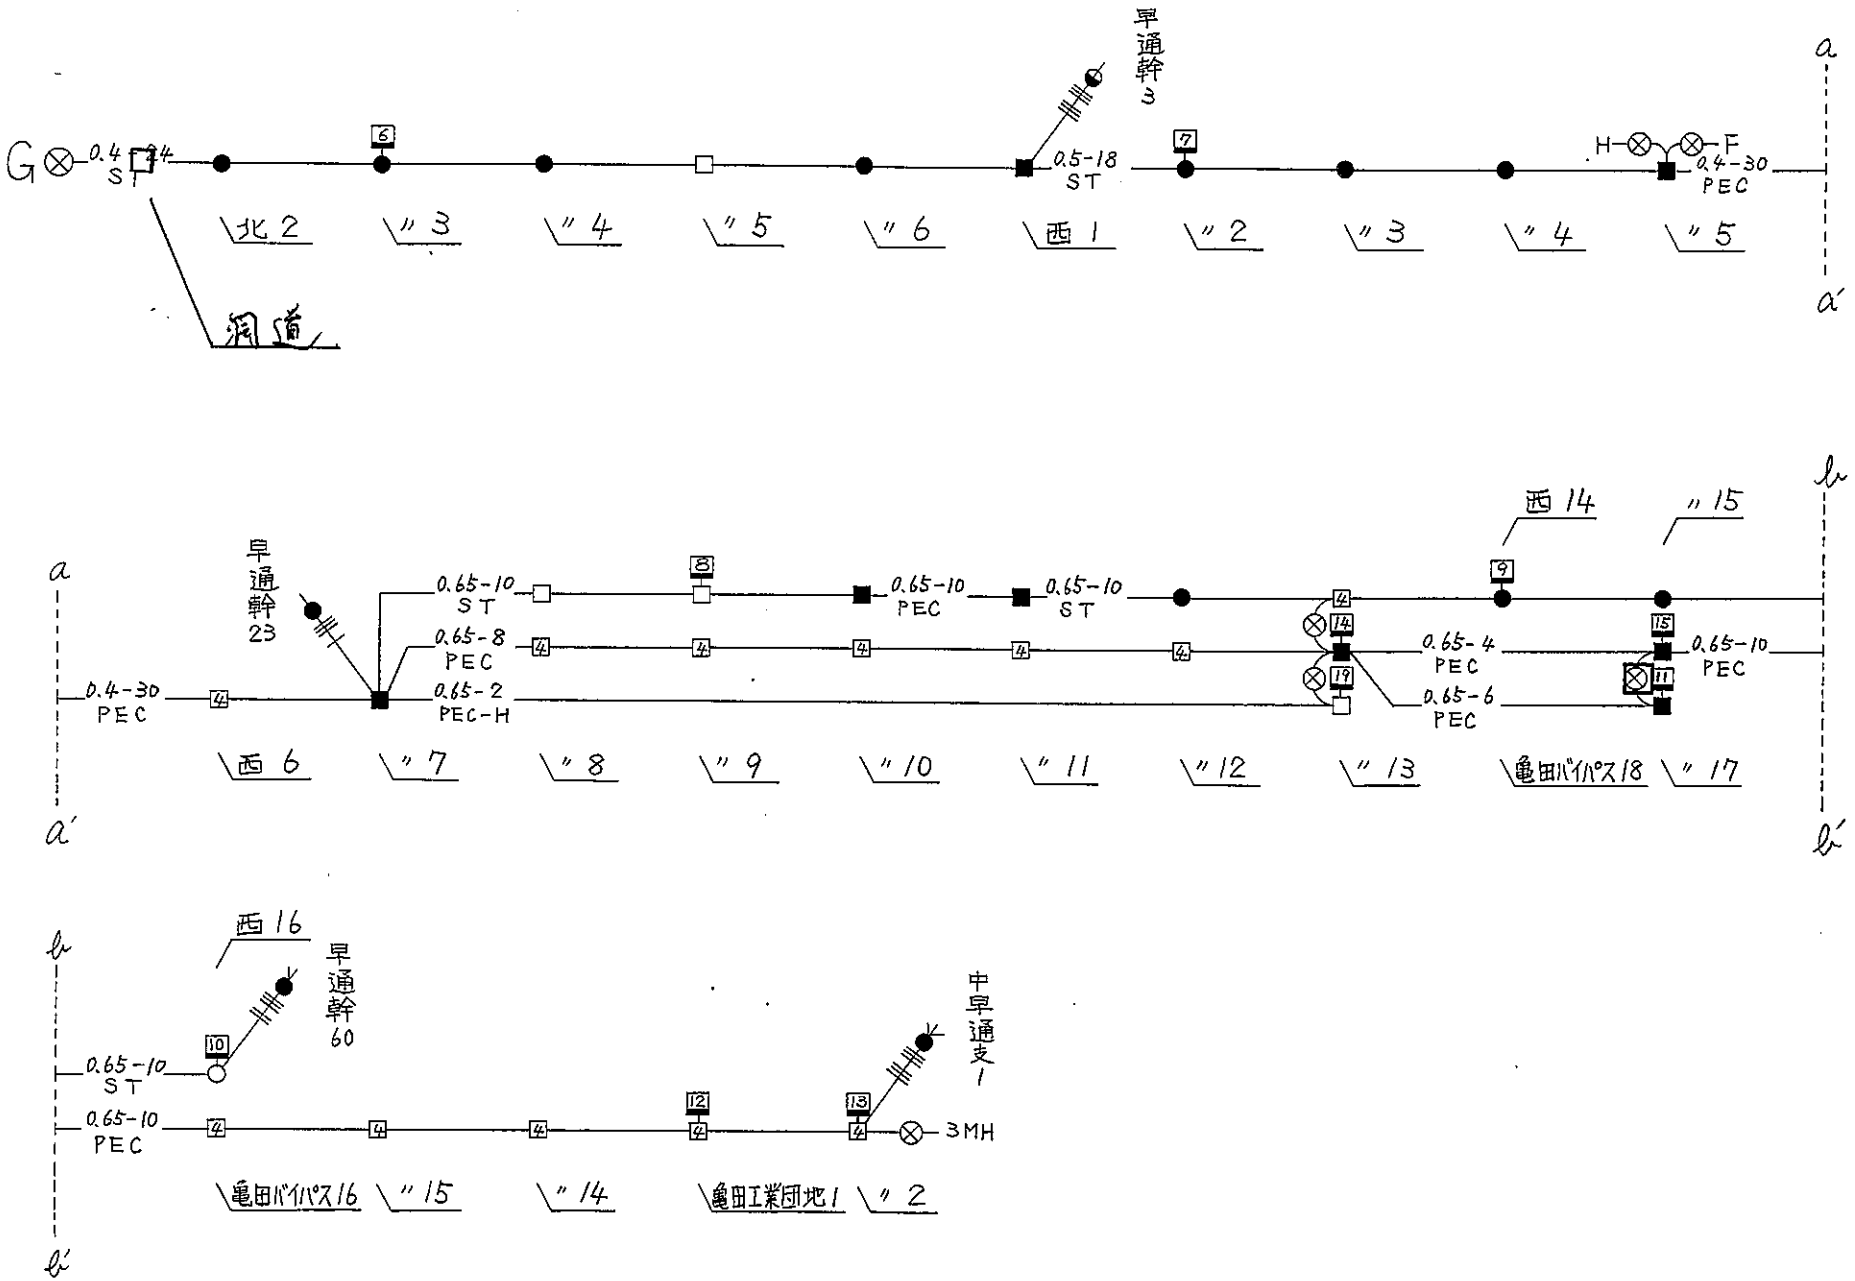
G
0.4 ST
24
6
北 2
〃 3
〃 4
〃 5
〃 6
洞道
早通幹 3
0.5-18 ST
7
西 1
〃 2
〃 3
〃 4
〃 5
H
F
0.4-30 PEC
a
a'
早通幹 23
0.4-30 PEC
4
0.65-10 ST
0.65-8 PEC
0.65-2 PEC-H
8
0.65-10 PEC
0.65-10 ST
9
西 14
〃 15
14
19
0.65-4 PEC
0.65-6 PEC
15
11
0.65-10 PEC
西 6
〃 7
〃 8
〃 9
〃 10
〃 11
〃 12
〃 13
亀田バイパス 18
〃 17
b
b'
西 16
早通幹 60
10
0.65-10 ST
0.65-10 PEC
12
13
中早通支 1
3MH
亀田バイパス 16
〃 15
〃 14
亀田工業団地 1
〃 2

亀田 G ケーブル